
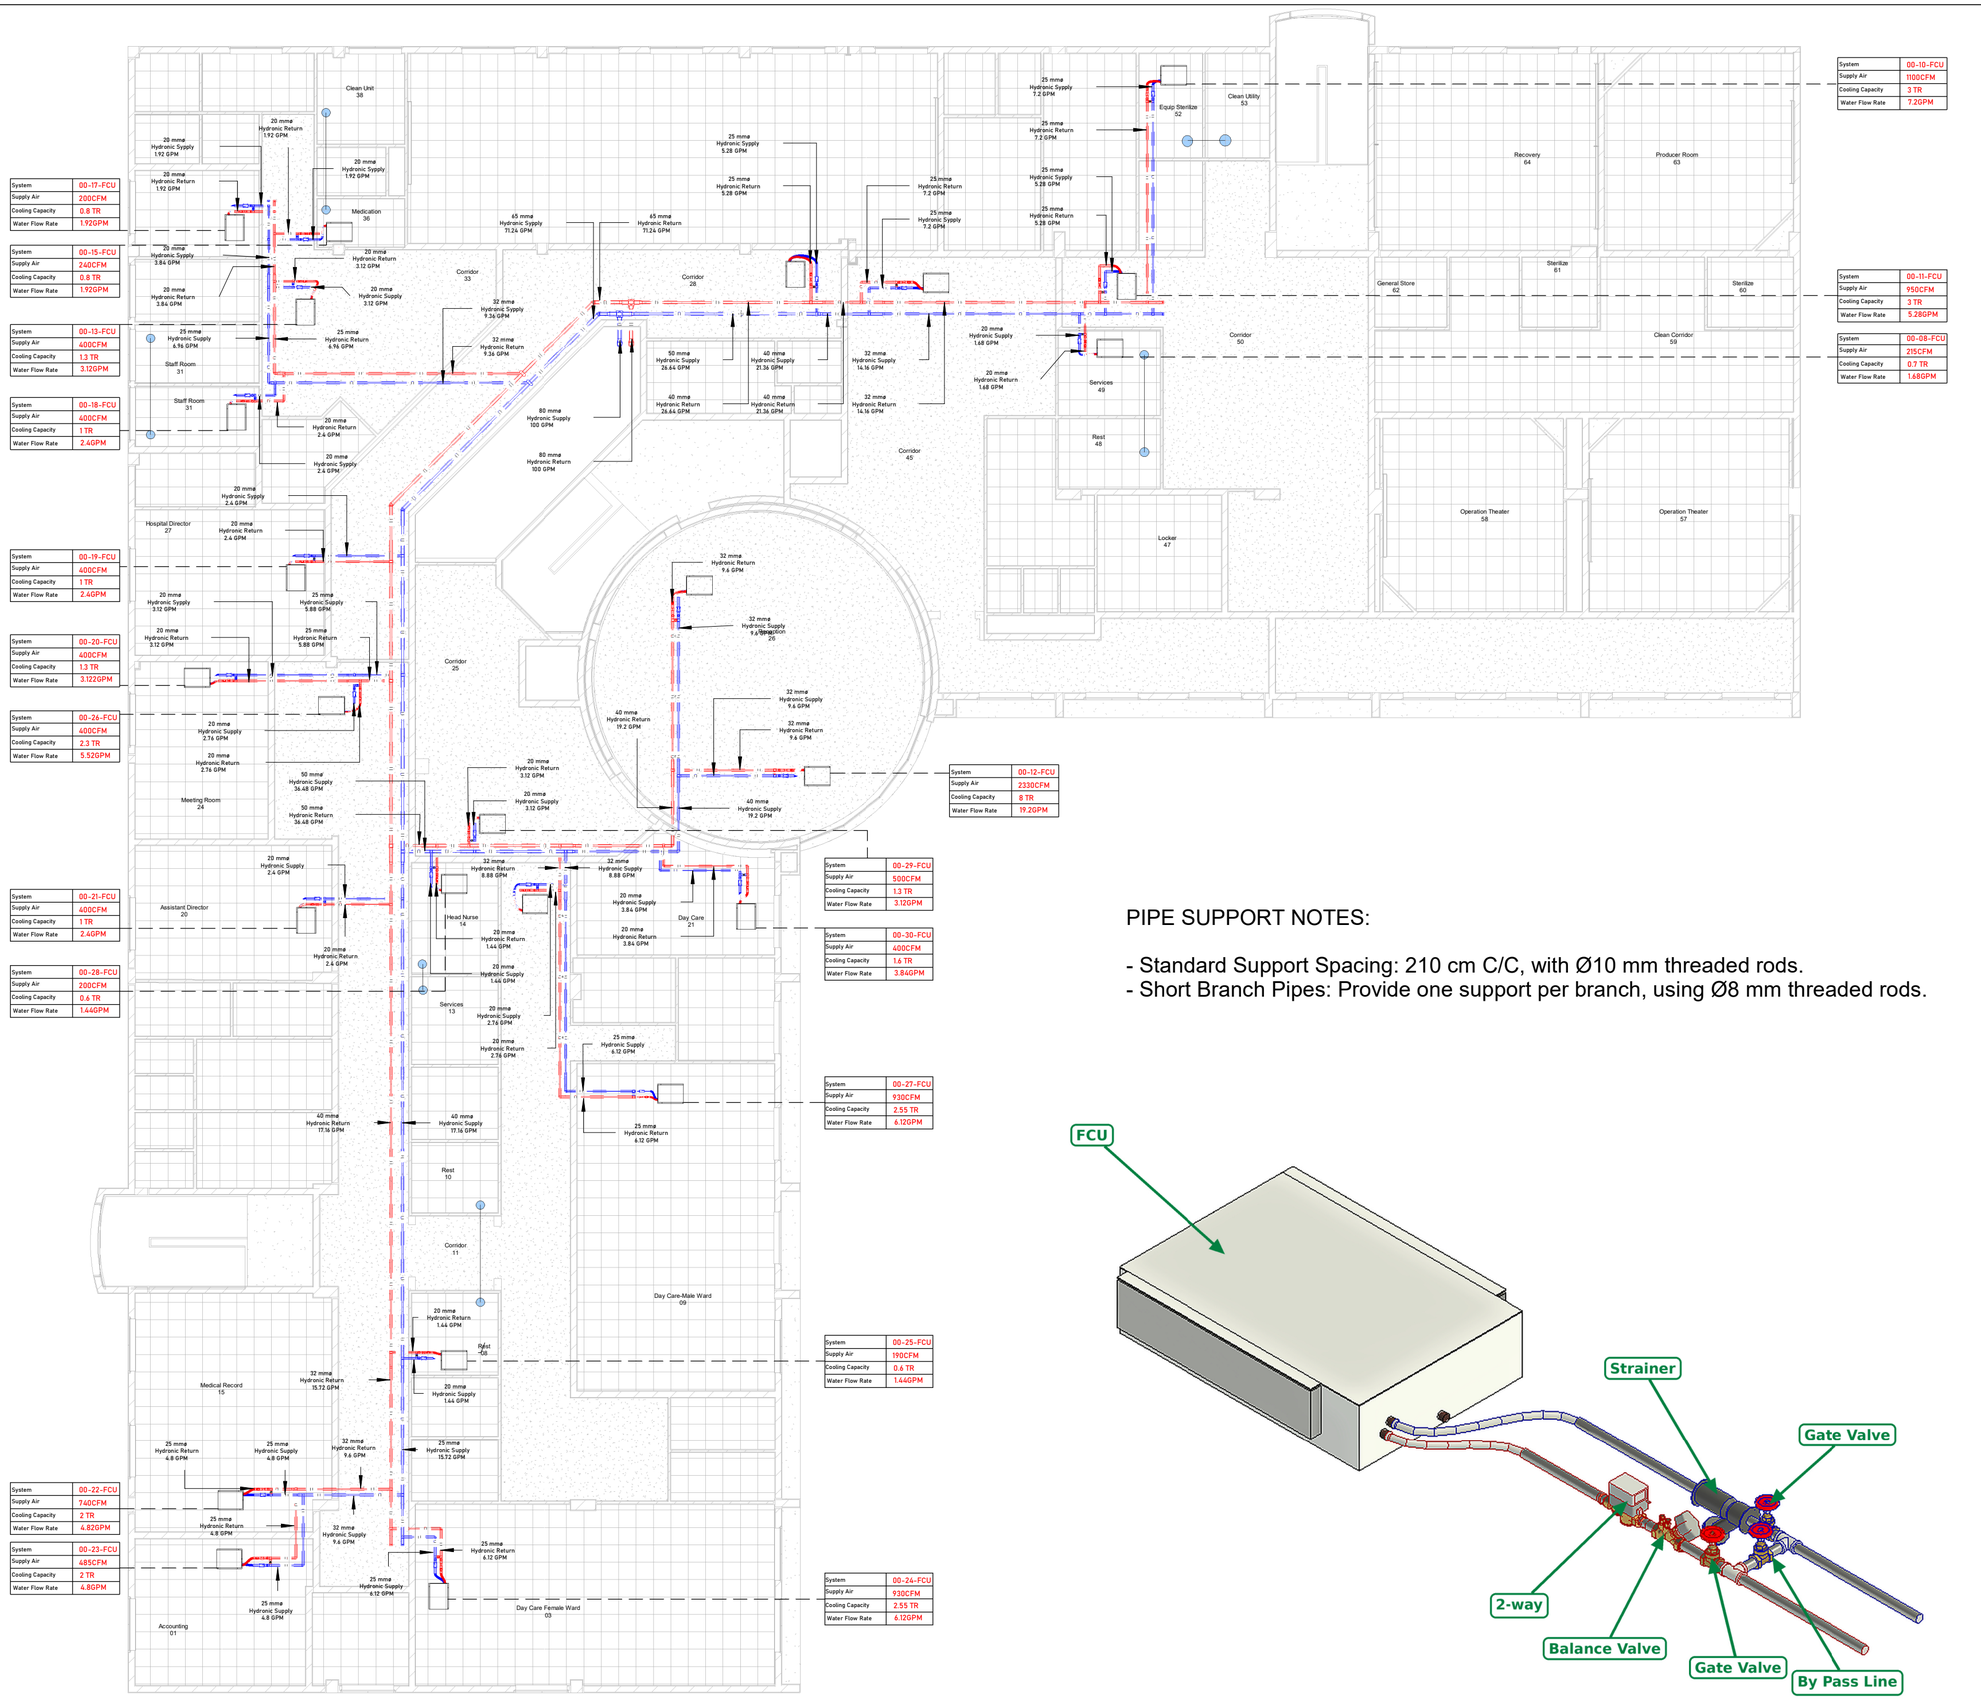




PIPE SUPPORT NOTES:

- Standard Support Spacing: 210 cm C/C, with Ø10 mm threaded rods.
- Short Branch Pipes: Provide one support per branch, using Ø8 mm threaded rods.

Key Plan

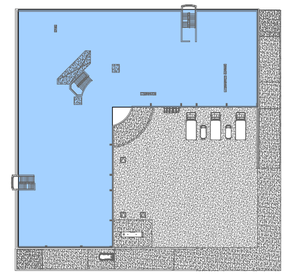

Legends:

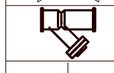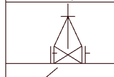	2_WAY
	Strainer
	Gate Valve
	Balancing Valve
	Fan Coil Unit
TR	Cooling ton
GPM	Gallons Per Minute
CFM	Cubic Feet per Minute
C/C	Center to Center

MOHAMED SHABAN
MECHANICAL ENGINEER

Project:	Hospital
Owner:	ENGX ENGINEERING TRAINING
Date:	17/10/2026
Designer:	M.Shaban
Checked by:	Taha Hussein
DRAWING:	Ground Floor
DISCIPLINE:	HVAC
Scale:	1:150